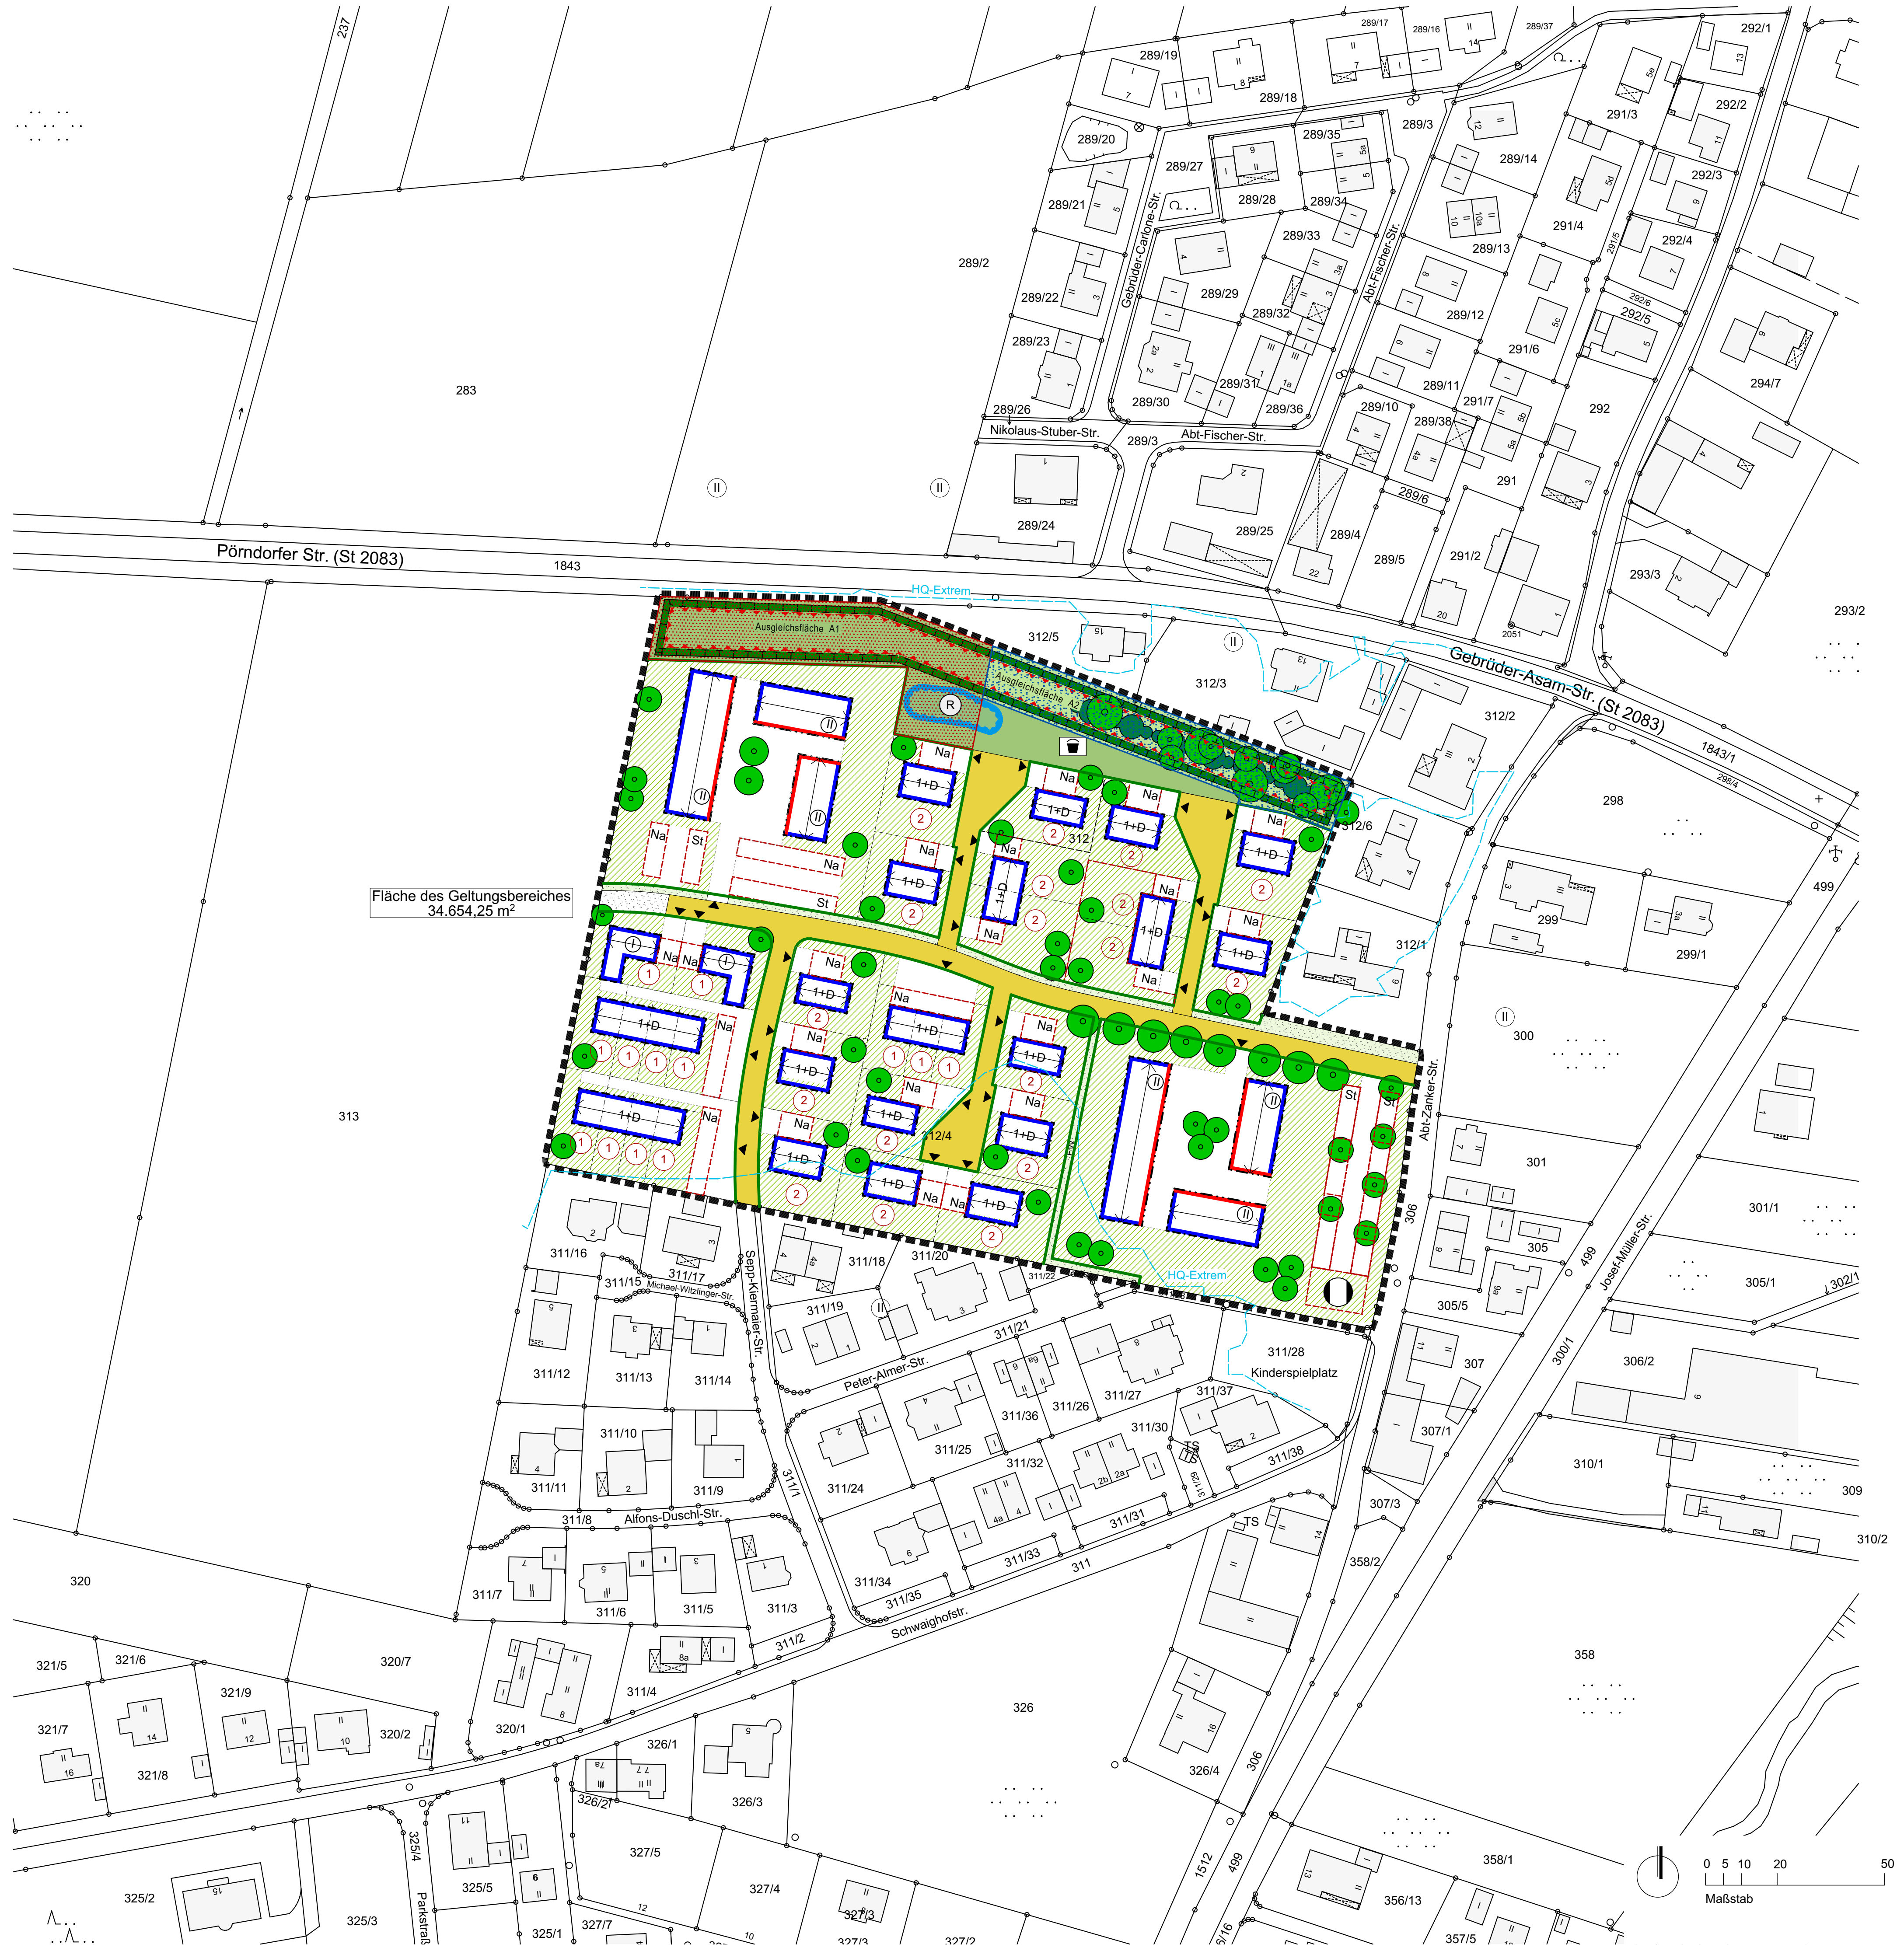

A Festzetzungen durch Planzeichnen

1. Art der baulichen Nutzung
(§ 9 Abs.1 Nr.1 BauGB, §§ 1 bis 11 BauNVO)

1.1 Wohnbaufläche

1.1.1 WA Allgemeines Wohngebiet (§ 4 BauNVO)

2. Maß der baulichen Nutzung
(§ 9 Abs.1 Nr.1 BauGB, § 16 BauNVO)

2.1 Grundflächenzahl GRZ 0,4 Dezimalzahl als Höchstmaß

2.2 Geschossflächenzahl GFZ 1,2 Dezimalzahl als Höchstmaß

2.3 Zahl der Vollgeschosse

2.3.1 (I) zwingend ein Vollgeschoss

2.3.2 (II) zwingend zwei Vollgeschosse

2.3.3 I+D mind. ein Vollgeschoss + Dachgeschoss
max. zwei Vollgeschosse

2.4 Höhe der baulichen Anlagen WH 6,5 Höchstmaß der Wandhöhe ggü. dem natürlichen Gelände

2.5 Anzahl der Wohneinheiten

2.5.1 ① max. 1 Wohneinheit

2.5.2 ② max. 2 Wohneinheiten

3. Bauweise, Baulinien, Baugrenzen
(§ 9 Abs.1 Nr.2 BauGB, §§ 22,23 BauNVO)

3.1 Bauweise Für das ganze Gebiet ist eine offne Bauweise vorgesehen

3.2 Baulinie gemäß § 23 (2) BauNVO

3.3 Baugrenze gemäß § 23 (3) BauNVO

3.4 Firstrichtung ⟷ Firstlinie zwingend in Pfeilrichtung

4. Versorgungs-, Gemeinbedarfs-, Sport- & Spielflächen
(§ 5 Abs.2 Nr. 2 und Abs. 4, § 9 Abs.1 Nr. 5 und Abs. 6 BauGB)

4.1 Spielanlagen

5. Verkehrsflächen (§ 9 Abs.1 Nr. 11 und Abs. 6 BauGB)

5.1 Straßenverkehrsflächen 🟨 öffentliche Straßenverkehrsflächen

5.2 öffentliche Fußwege FW öffentlicher Fußweg in wassergebundenem Belag, Mineralbeton

5.3 Straßenbegrenzungslinie

5.4 Ein- bzw. Ausfahrten ▼

6. Grünflächen (§ 9 Abs.1 Nr. 15 und Abs. 6 BauGB)

6.1 Grünflächen

🟩 öffentliche Grünflächen

▨ private Grünflächen

▨ interne Ausgleichsfläche (A1)

▨ interne Ausgleichsfläche (A2)

7. Wasserflächen, Flächen f. Wasserwirtschaft, Hochwasserschutz und die Regelung des Wasserabflusses
(§ 5 Abs.2 Nr. 7 und Abs. 4, § 9 Abs.1 Nr. 16 und Abs. 6 BauGB)

7.1 Retentionsbecken (R) Umgrenzung von Flächen für die wasserwirtschaft, den Hochwasserschutz und die Regelung des Wasserabflusses

8. Flächen z. Schutz, Pflege und Entwicklung von Natur und Landschaft
(§ 5 Abs.2 Nr. 10 und Abs. 4, § 9 Abs.1 Nr. 20, 25 und Abs. 6 BauGB)

8.1 Umgrenzung von Flächen für Maßnahmen zum Schutz, zur Pflege und zur Entwicklung von Natur und Landschaft
(§5 Abs. 2 Nr. 10 Abs. und Abs. 4, § 9 Abs. 1 Nr.20 und Abs. 6 BauGB)

Schutzfläche gem. textl. Festsetzungen – Flächen für Maßnahmen zum Schutz, zur Pflege und zur Entwicklung von Natur und Landschaft

8.2 Anpflanzungen von Bäumen, Sträuchern und sonstigen Bepflanzungen und für die Erhaltung von Bäumen, Sträuchern und sonstigen Bepflanzungen sowie von Gewässern

Gehölze zu pflanzen (§9 Abs.1 Nr. 25a BauGB)	Gehölze Bestand zu erhalten (§9 Abs.1 Nr. 25a BauGB)
● Bäume 1. Ordnung	● Bäume 1. Ordnung
● Bäume 2. Ordnung	● Bäume 2. Ordnung
	Heckenbereiche (A2)

9. Sonstige Planzeichen

9.1 Umgrenzung von Flächen für Nebenanlagen, Stellplätze, Garagen und Gemeinschaftsanlagen (§ 9 Abs. 1 Nr. 4)

Nebenanlagen

Na – Nebenanlagen, zulässig sind: Garage, Carport, Müllraum, Abstellraum

St – private Stellplatzfläche in wasserdurchlässigen Belägen

9.2 Umgrenzung der Flächen für Lärmschutz Vorkehrungen zum Schutz gegen schädliche Umwelteinwirkungen im Sinne des Bundes-Immissionsschutzgesetzes
(§ 9 Abs. 1 Nr. 24 und Abs. 6 BauGB)

9.3 Geltungsbereich – Grenze des Räumlichen Geltungsbereichs, (§9 Abs. 7 BauGB)

B Hinweise durch Planzeichen

1078 – Flurgrenze mit Flurstücksnummer

Vorgeschlagene Grundstücksgrenze

Versorgungsanlage Fernwärme

HQ Extrem Linie; n. Auskunft WWA

C Festsetzungen durch Text

1. Bebauung

1.1. Bauweise
Nach Eintragung in der Planzeichnung wie folgt:

1.1.1. offene Bauweise nach §22 Abs. 2 BauNVO

1.2. Bauliche Anlagen: Allgemeine Festsetzungen
(gem. Art. 81 BayBO)

1.2.1. Dachform und Dachdeckung.
Hauptgebäude: Zulässig sind nur symmetrische Satteldächer, Flachdächer und Pultdächer. Die zulässige Dachneigung bei Satteldächern beträgt 15-22° mit durchgehender Trauf- und Firstlinie. Die Zulässige Dachneigung bei Pultdächern beträgt 5-20°.
Zulässige Eindeckung: naturrote oder anthrazitfarbene Dachsteine oder Blecheindeckungen bei Pult- und Satteldächern, Dachbegrünung bei Flachdächern.
Nebengebäude und eingeschossige Gebäudeteile: Zulässig sind nur extensiv begrünte Flachdächer und flache Blechdächer (Neigung 5-10°).

1.2.2. Gauben, Zwerchgiebel bei I+D
Gauben und Zwerchgiebel sind nicht zulässig außer bei Gebäuden mit einer zulässigen Geschossigkeit von I+D. Dachflächen sind ansonsten als ruhige Flächen auszubilden: Dachaufbauten, Dachlaternen, Quergiebel, Negativeinschnitte und dgl. sind nicht zulässig.

1.2.3. Außenwandgestaltung
Zulässig sind Putzflächen, Holzschalungen sowie hinterlüftete Bekleidungen aus Faserzementplatten.

1.2.4. Photovoltaik / Solaranlagen
Aufständerungen von Solaranlagen sind nicht zulässig. Ein Überstand der Solarmodule über die Dachhaut ist nicht zulässig.

1.2.5. Grenzwände
sind als Schildwände auszubilden. Sie sind min. 30 cm über die Oberkante der Dacheindeckung zu führen und oberseitig mit Blechabschluss einzudecken.

1.2.6. Höhenbezug / Wandhöhen
Unterer Höhenbezugspunkt für Wandhöhen von Gebäuden ist die OKFF EG.
Die OKFF ist so zulegen, dass sie 30 cm über der OK der an den Grundstücksgrenzen anliegenden Bordsteinhöhe liegt. Als Wandhöhe gilt das Maß von der OKFF EG bis zum Schnittpunkt der Außenwand mit der Dachhaut, traufseitig gemessen.

1.3. Zahl der Wohneinheiten
Die Zahl der zulässigen Wohneinheiten wird begrenzt und ist in die jeweilige Parzelle eingetragen.

1.4. Abstandsflächen
Die Abstandsflächen gem. Art. 6 Abs. 5 Satz 1 BayBO sind einzuhalten.

1.5. Nebenanlagen,

1.5.1. Carports, Garagen, Nebengebäude:
Carports und Garagen sind nur innerhalb der dafür ausgewiesenen Flächen und innerhalb der überbaubaren Grundstücksfläche zulässig. Stellplätze dürfen auf den ausgewiesenen Flächen sowie vor den Carport/Garagenstellplätzen errichtet werden.
Maximal zulässige Wandhöhe der Nebenanlagen: 3,0m über dem natürlichen Gelände.
Garagenvorplätze und Stellplätze dürfen zur Straße hin nicht eingezäunt werden und sind über die gesamte Breite mit wasserdurchlässigen Belägen zu versehen.

1.5.2. Stellplatznachweis
Für die Anzahl der erforderlichen Stellplätze gelten die Bestimmungen der Garagen- und Stellplatzverordnung (mind. 1 Stellplatz je Wohnung).

1.5.3. Müllunterbringung
Selbstständige bauliche Anlagen zur Müllunterbringung sind nicht zulässig. Bauliche Anlagen zur Müllunterbringung sind in die Gebäude zu integrieren.

1.6. Einfriedungen

1.6.1 Zäune

1.6.1.1 Arten
Zulässig sind Holzzäune, Maschendrahtzäune, Einstab- und Doppelstabmatten und Schmiedezäune.
Sockelmauern und Stacheldrahtzäune in jeglicher Form sind unzulässig.

1.6.1.2 Höhe
An Straßenseiten max. 1,20 m über Straßen- bzw. Bürgersteigoberkante. Eine Hinterpflanzung der Zäune ist zulässig, es muss jedoch ein ungehindertes Ein- und Ausfahren aus den Grundstücken (Stellplätze), auch aus den Nachbargrundstücken gewährleistet sein.
Bei Grundstücken, die im Bereich von Einmündungen an Straßen des überörtlichen Verkehrs angrenzen, dürfen nur Zäune bis 0.80 m Höhe errichtet werden (Sichtdreieck).
Zwischen den Grundstücken ist eine maximale Zaunhöhe von 1,20 m zulässig.
Eine Hinterpflanzung der Zäune ist wünschenswert. Es wird hierbei auf Art. 47 AGBGB und den Grünordnungsplan verwiesen.

1.6.1.3 Ausführung

1.6.1.3.1 Holzzaun
Unzulässig sind blickdichte Zaunelemente, sowie Elemente, welche eine wandartige Wirkung erzeugen.

1.6.1.3.2 Maschendrahtzaun
Mit Pfosten aus Rohr- oder Winkelstahl (in kleinen Querschnitten) tannengrün oder graphitfarben gestrichen, mit durchlaufendem Drahtgeflecht zu errichten.

1.6.1.3.3 Einstab- und Doppelstabmatten, Schmiedezäune
Tannengrün, graphitgrau oder verzinkt

1.6.2 Pfeiler
Zulässig aus verputztem Mauerwerk oder Naturstein, max. 0,20 m breit und 0,20 m tief.
Die Zaunhöhe darf nicht überschritten werden. Bei Eingangs- und Einfahrtstoren sind Pfeiler mit einer max. Breite von 0,5 m und einer Tiefe von 0,4 m zulässig.
Die Zaunhöhe darf nicht überschritten werden.

1.6.3 Mauern
Mauern jeglicher Art sind als Einfriedung unzulässig.

1.6.4 Stützmauern
Stützmauern sind bei Grundstücken,

- in Höhe von 0,60 m zulässig, wenn das natürliche Gelände über eine Länge von 20 m mindestens 1 m abfällt
- in Höhe von 0,80 m zulässig, wenn das natürliche Gelände über eine Länge von 10 m mindestens 1 m abfällt

(Abgrabung: gemessen von OK geplantes Gelände bis OK-Mauer;
Aufschüttung: gemessen von OK-Urgelände bis OK-Mauer).
Die Gesamtlänge der Stützmauern darf 30 m auf dem bebauten Grundstück nicht überschreiten.
Mit aufgesetztem Zaun darf die Gesamthöhe von 1,70 m nicht überschritten werden (Abgrabung: gemessen von OK geplantes Gelände bis OK-Zaun;
Aufschüttung: gemessen von OK-Urgelände bis OK-Zaun).

Im Bereich von Einmündungen ist eine max. Höhe (Abgrabung: gemessen von OK geplantes Gelände bis OK-Zaun; Aufschüttung: gemessen von OK-Urgelände bis OK-Zaun) von nur 0,40 m zulässig (Sichtdreieck).
Das Gelände darf in seinem natürlichen Verlauf nicht unnötig gestört oder verändert werden. Die Höhenunterschiede sind, wenn möglich durch Böschungen auszugleichen.
Ist im Ursprungsbebauungsplan oder einem bereits rechtskräftigen Deckblatt eine Ortsrandeingrünung oder sonstige Bepflanzung vorgesehen, so ist die Stützmauer mit Hecken und / oder Sträuchern zu hinterpflanzen.

1.6.5 Sichtschutzelemente
Zulässig sind Sichtschutzelemente aus Holz, Gabionen und Naturstein.
Eine Unterteilung ist erwünscht.

1.6.5.1 Höhe
max. 2 m, gemessen ab OK-Gelände bis OK-Sichtschutzwand

1.6.5.2 Länge
max. 9 m, jedoch nur an einer seitlichen oder rückwärtigen Grundstücksgrenze (nicht an eine öffentliche Straße grenzend) zulässig.

1.7. Abgrabungen / Aufschüttungen / Stützmauern
Abgrabungen und Aufschüttungen sind bis max. 1,0 m unter/über natürlichem Gelände zulässig. Stützmauern sind bis zu einer Höhe von 1,0 m zulässig. An angrenzende Verkehrsflächen und Nachbargrundstücke ist höhengleich anzuschließen.

1.8. Werbeanlagen
Im gesamten Planungsgebiet sind Werbeanlagen nicht zulässig.

1.9. Bruttogrundfläche
Die Mindestgrundfläche pro Wohnhaus beträgt 60 m² BGF.

1.10. Lärmschutz

1.10.1 *Im Norden der Fläche muss eine Kombination aus Lärmschutzwall (Oberkante 327,10 ü. N. N.) und Lärmschutzwand (Oberkante 328,60 ü. N. N.) vor der Aufnahme der Wohnnutzung errichtet werden.*

1.10.2 *Schutzbedürftige Räume gemäß DIN 4109 (Schallschutz im Hochbau – Teil 1: Mindestanforderungen, Stand Januar 2018) dürfen nur innerhalb des grünen (≤ 49 dB) Bereiches ohne weitere Vorkehrungen errichtet werden. Innerhalb des roten Bereiches (≤ 49 dB) müssen ausreichend lärmmindernde Maßnahmen (z.B. Laubengang, Glaselemente, Hafencity-Fenster) vorgebaut werden. Ist dies aus baulicher oder planerischer Sicht nicht möglich, müssen Fenster von schutzbedürftigen Räumen, insbesondere Fenster von Schlaf- und Kinderzimmern, mit einer fensterunabhängigen Lüftungseinrichtung ausgestattet werden, sodass ein Öffnen der Fenster für Belüftungszwecke nicht zwingend notwendig ist.*

EG

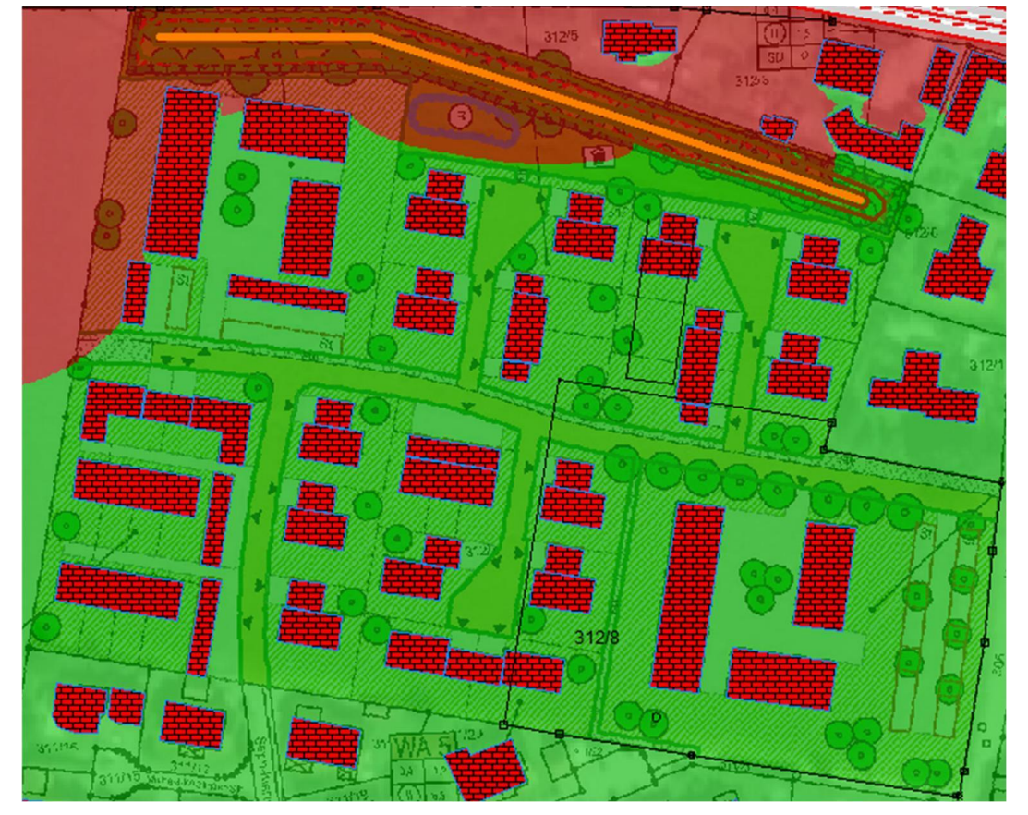

OG

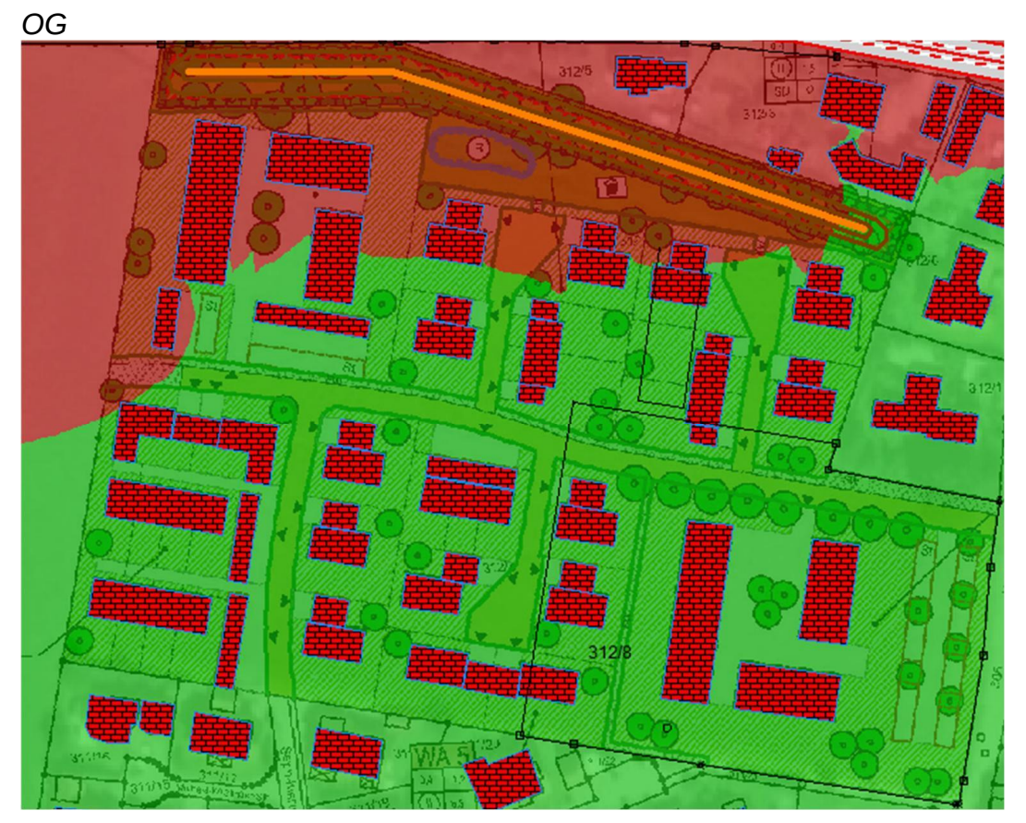

1.10.3 *Aufenthaltsbereiche im Freien (Balkon, Terrasse) sind im roten Bereich auf der Fassadenseite, ohne direkte Sichtverbindung zur Straße anzuordnen. Alternativ können diese mit ausreichend lärmabschirmenden Maßnahmen (geschlossenen Brüstungen, Glaselemente, etc.) errichtet werden.*

EG

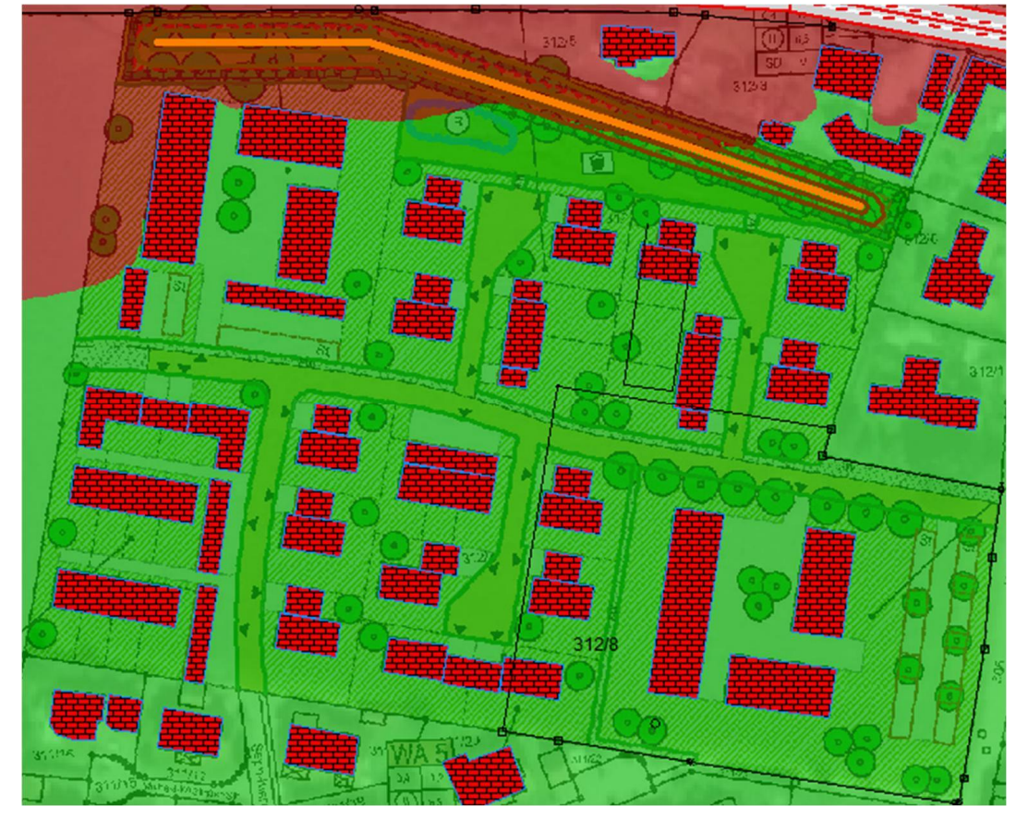

OG

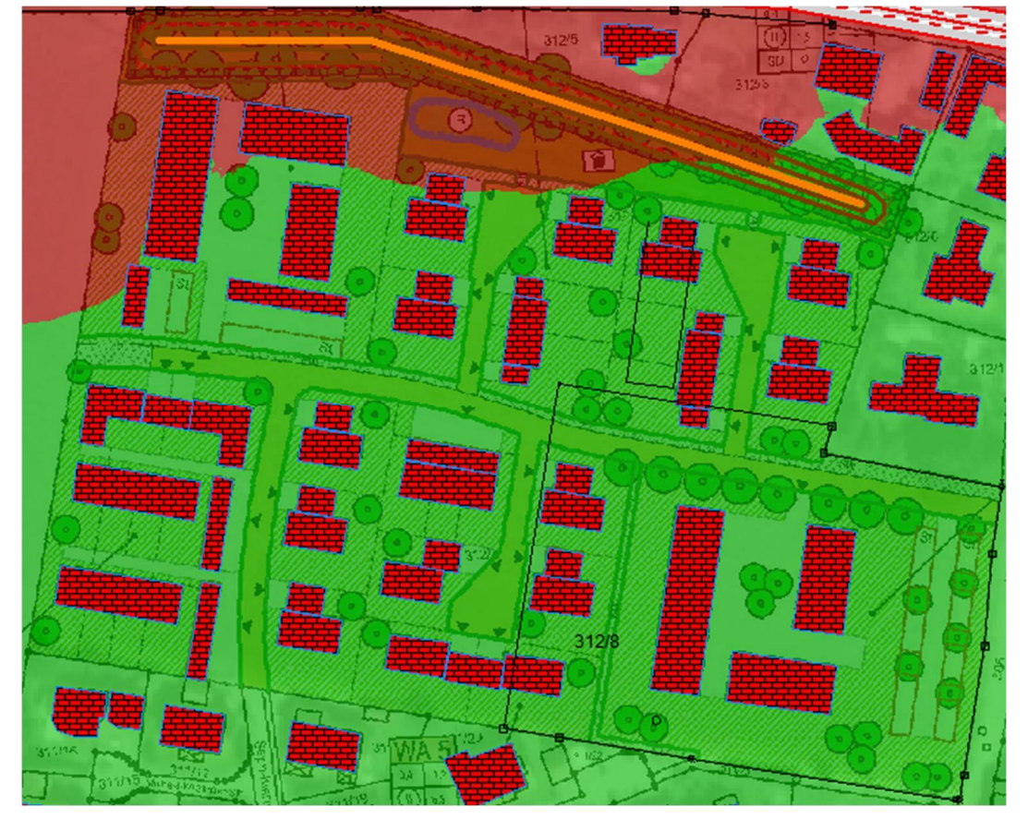

1.10.4 *Bei der Errichtung von schutzbedürftigen Räumen im Sinne der DIN 4109 (Büroräume, Aufenthaltsräume etc.) ist durch den Bauherrn ein Nachweis der Anforderungen der DIN 4109 zu erbringen. Der Nachweis ist nach der jeweils bauaufsichtlich eingeführten Fassung der DIN 4109 zu führen und im Zuge des Baugenehmigungsverfahrens der Genehmigungsbehörde vorzulegen.*

2. GRÜNORDNUNG

2.1. ALLGEMEINE
Die Vegetationsflächen sind entsprechend den planliche und textlichen Festsetzungen anzulegen, zu sichern und dauerhaft zu erhalten. Ausbleibende Pflanzen sind zu ersetzen. Die Vegetationsflächen sind spätestens in der Pflanzperiode nach Erstellung der Erschließungsflächen und nach Nutzungsaufnahme/-beginn der Gebäude fertigzustellen. Nach- und Ersatzpflanzungen haben den Pflanzqualitäten des Grünordnungsplanes zu entsprechen. Die Pflanzqualitäten müssen den Gütebestimmungen des Bundes deutscher Baumschulen (BdB) entsprechen.
Für die im Plan festgesetzten Neuanpflanzungen von Gehölzen in den privaten Vegetationsflächen wird die Verwendung der in Punkt 2.4.1.ff ausgewiesenen Gehölze festgesetzt.
Für weitere Planungen können alle Ziergehölze verwendet werden, außer die in Punkt 2.4.4. beschriebenen Arten.
Für freiwachsende Hecken und Gehölzgruppen:
Pflanzdichte 1 Stück/1,50 qm
Pflanzqualitäten:
Bäume I. Ordnung: Hochstamm, 3xv., STU 18 - 20 cm
Bäume II. Ordnung: Hochstamm, 3xv., STU 16 - 18 cm oder Heister, 2xv., 150 - 200 cm
Sträucher: 2xv., 100 - 150 cm bzw. 60 - 100 cm

2.2. ÖFFENTLICHES GRÜN
Öffentliche Grünflächen sind nach Plandarstellung mit artenreichen Wiesen (Lebensraumtyp 6510) anzusäen. Pflanzungen auf öffentlichen Grünflächen sind entsprechend der angefügten Pflanzlisten ausschließlich mit autochthonen Pflanzen herzustellen. s. Festsetzung 2.4 ff.

2.3. PRIVATES GRÜN
Die im Planausschnitt M 1:1000 vorgesehenen Baumreihen entlang der internen Erschließungsstraßen, sowie für die interne Erschließung bis zu den geplanten Wendehämmern, weiterhin die privaten Grundstücke des Allgemeinen Wohngebietes müssen umgesetzt werden. Von den dargestellten Standorten darf in geringem Maß abgewichen werden. (Max. 5m)
Geschlossene Pflanzflächen sind mit heimischen Sträuchern dicht anzupflanzen. Je 1,5 qm 1 Strauch, je 250 qm Grundstücksfläche ist mindestens 1 heimischer Großbaum zu pflanzen die am Straßenraum liegenden Pflanzen können nicht angerechnet werden, diese müssen zusätzlich gepflanzt werden. Pflanzlisten siehe 2.4 ff.

2.4. PFLANZLISTE FÜR PRIVATE/ÖFFENTLICHE GRÜNFLÄCHEN

Auswahlliste für straßenraumbegleitende Bäume entlang Erschließungsstraßen

2.4.1. BÄUME I. ORDNUNG

Acer platanoides in Sorten, Spitz-Ahorn in Sorten
Ulmus x hollandica „Lobel“, Schmalkronige Stadtulme
Tilia cordata „Greenspire“, Amerikanische Stadtlinde

BÄUME II. ORDNUNG
Prunus avium in Sorten, Vogel-Kirsche in Sorten
Acer campestre „Elsrijk“, Feld-Ahorn „Elsrijk“

Auswahlliste allgemein für private/öffentliche Grünflächen

2.4.2. BÄUME I. ORDNUNG

Acer platanoides, Spitz-Ahorn
Acer pseudoplatanus, Berg-Ahorn
Tilia cordata, Winter-Linde
Quercus robur , Stiel-Eiche

BÄUME II. ORDNUNG
Acer campestre, Feld-Ahorn
Carpinus betulus, Hainbuche
Crataegus carrierei, Apfel-Dorn
Malus domestica, Wild-Apfel
Prunus avium in Sorten, Vogel-Kirsche, auch in Sorten
Prunus padus, Trauben-Kirsche
Sorbus aucuparia, Eberesche

alle Obst- und Nußbäume (Mindest-Pflanzqualität: Halbstamm)
Obstbäume: alle standortgerechten, regionaltypischen Arten und Sorten
Walnuss: als Sämling
Verwendung für interne Ausgleichsflächen / Ortsrandeingrünung

2.4.3. HEIMISCHE STRÄUCHER

Cornus sanguinea, Hartriegel
Corylus avellana, Hasel
Cornus mas, Kornelkirsche
Lonicera xylosteum, Heckenkirsche
Ligustrum vulgare, Liguster
Prunus spinosa, Schlehe
Rosa canina, Hunds-Rose
Salix caprea, Sal-Weide
Sambucus nigra, Holunder
Viburnum opulus, Gemeiner Schneeball
Viburnum lantana, Wolliger Schneeball

In den Freiflächen ohne Pflanzauflagen und um die Gebäude sind ergänzend für strauchartige und bodenbedeckende Bepflanzungen Ziersträucher zugelassen.

2.4.4. UNZULÄSSIGE PFLANZENARTEN

Landschaftsfremde Baumarten wie Edeltannen und Edelfichten, Zypressen, Thujen usw. sowie alle Trauer- und Hängeformen (in allen Arten und Sorten), dürfen nicht gepflanzt werden.

2.5.INTERNE AUSGLEICHSFLÄCHE (A1)

Entwicklungsziel

Ziel der Ausgleichsfläche ist es auf der Vorhabenfläche eine artenreiche Flachlandmähwiese n. LRT (Lebensraumtyp) 6510 zu entwickeln. Der Lebensraumtyp wird definiert als artenreiche, extensiv bewirtschaftete Mähwiese im Flach- und Hügelland. Dies schließt sowohl trockene als auch frisch-feuchte Mähwiesen ein. Die Glatthafer- oder Goldhaferwiese bieten einer Vielzahl von Kräutern, durch den lückigen Aufbau, und einer ausgeprägten Vertikalstruktur Lebensraum für viele Tierarten insbes. für Tagfalterarten. Ausschlaggebend hierbei ist das Magerkeitsanzeiger weitgehend fehlen.

Entwicklung - Anlage und Pflege
Eine mind. 3malige Mahd mit Abfuhr des Mahdgutes in den ersten beiden Vegetationsperioden wird angeregt. Nach den beiden Jahren der Aushaagerung ist mittels Mahdguttransfer aus Spenderflächen oder die Verwendung von gebietseigenem Saatgut der Ursprungsregion UG16 die Wiese zu belegen oder anzusäen.
Das Mahdgut (beim Mahdguttransfer) muss hierbei ausgebracht und zur Aussammung gewendet werden. Dieser Vorgang ist weitere 2 Vegetationsperioden durchzuführen.
Bei Ansaat ist die Fläche anzusäen und entsprechend vorher vorzubereiten. Sollte der Aufwuchs nicht den gewünschten Deckungsgrad bringen, so kann im darauffolgenden Jahr nochmals eine Ansaat erfolgen.
Nach Initialisierung und Aufwuchs der gewünschten Arten ist die Fläche dann dauerhaft 2malig im Jahr zum Mähen. 1. Mahd nicht vor dem 15. Juni; 2. Mahd im September jeden Jahres; Das Mahdgut ist dabei immer abzufahren. Für die optimale Entwicklung der Wiesenflächen ist es essenziell das auf jedwege Düngerzugabe und Behandlung von Pflanzenschutzmittel verzichtet wird. Nach ca. 7 Jahren sollte dann bereits der gewünschte Lebensraumtyp etabliert sein.

2.6.INTERNE AUSGLEICHSFLÄCHE (A2)

Entwicklungsziel
Im Bereich der St 2083 ist im Nordöstlichen Bereich eine wärmeliebende Hecke mit Bäumen zu pflanzen. Pflanzdichte und zu verwendende Arten sind den Pflanzlisten, Punkt 2.4 ff. zu entnehmen. Die Hecke ist in diesem Bereich mindestens 3-reihig zu pflanzen.
Entwicklungsziel ist eine mesophile Hecke nach dem Biotopty B112 der BayKompV.
Die ersten beiden Jahre ist die Pflanzung mindestens 2mal jährlich freizuschneiden, so dass die Sträucher und Bäume ungestört anwachsen und durchtreiben können. (Es wird generell ein Verbissschutz angeregt oder die Einzäunung der Heckenbereiche während der Entwicklungsphase). Nach den ersten beiden Vegetationsperioden ist die Mahd auf einmalig im Jahr umzustellen, wobei das Mahdgut immer abgefahren werden muss. Ein Schnitt (außer Schulungsschnitte) wird generell untersagt. Die Verwendung von Pflanzenschutzmittel wird generell untersagt.

2.7. NUTZUNG VON REGENWASSER
Das anfallende Regenwasser auf den Grundstücken ist zu sammeln und wiederzuverwenden. Hierzu muss jede Einfamilienhaus- Doppelhaus- und Reihenhausparzelle eine mindestens 5 m³ fassende Zisterne vorhalten. Die im Nord-Westen und Süd-Osten gelegenen Wohnhöfe müssen jeweils Zisternen mit einem Fassungsvermögen von 20 m³ vorhalten.

2.8. REGENRÜCKHALTEBECKEN
Zur Sicherung des geregelten Regenwasserabfluss wird am Abschluss des Baugebietes ein Regenrückhaltebereich für Versickerung vorgesehen. Der Notüberlauf der Anlage wird an einen bestehenden Graben angeschlossen.

2.9. ANSAATEN IN PRIVATGARTENBEREICHE
Innerhalb der privaten Grünflächen ist ein Sport- und Spielrasen zulässig. Es wird angeregt Teile der Flächen auch mit Blühwiesen anzulegen, um eine Artenanreicherung innerhalb des Gebietes zu erreichen.

2.10. LAGE VON VER- UND ENTSORGUNGSLEITUNGEN
Die festgesetzten Pflanzflächen sind von Ver- und Entsorgungsleitungen (Strom, Wasser, Abwasser, Telekom, Gas etc.) ausdrücklich freizuhalten, um die Pflanzung und den langfristigen Erhalt der geplanten Gehölze zu gewährleisten. Die jeweiligen Abstände nach den entsprechenden Richtlinien sind einzuhalten.
Bei Pflanzung im Bereich von bestehenden Ver- und Entsorgungsleitungen sind nur flachwurzelnde Sträucher zu verwenden. Bäume und tiefwurzelnde Sträucher sind nicht erlaubt. Bei Baumpflanzungen ist ein Mindestabstand von je 2,50 m beiderseits von Kabeltrassen freizuhalten, ansonsten sind entsprechende Schutzmaßnahmen durchzuführen.

2.11. PFLANZENBEHANDLUNGSMITTEL
Der Einsatz von Herbiziden, Pestiziden und mineralischen Düngemitteln ist auf den festgesetzten Vegetationsflächen zum Schutz des Grundwassers sowie von Tieren und Pflanzen und im Hinblick auf eine möglichst standortgemäße und naturnahe Artenzusammensetzung nicht zulässig.

HINWEISE

1. STELLPLÄTZE
Die notwendige Anzahl der Stellplätze ist nach GaStellV zu bemessen.

2. SCHUTZ DES MUTTERBODENS NACH § 202 BAUGB
Vor jeder Baumaßnahme ist der anstehende Oberboden insgesamt zu sichern und zur Wiederverwendung zwischenzulagern (DIN 18915). Die Humusmieten sind mit Leguminosen zu begrünen.

3. PFLANZLISTE / SCHUTZ DER KINDER
Zum Schutz der Kinder ist bei der Bepflanzung des Spielplatzes auf Pflanzen zu verzichten, die in der beim Giftinformationszentrum (GIZ) Nord verfügbaren Liste der giftigen Pflanzen aufgelistet sind. Die Liste kann Online abgerufen werden unter: https://www.giz-nord.de/cms/indes.php/liste-giftiger-pflanzenarten.html.

4. ANGRENZENDEN LANDWIRTSCHAFT
Die durch die ordnungsgemäße Bewirtschaftung der angrenzenden landwirtschaftlichen Nutzfläche auftretenden Immissionen in Form von Geruch, Staub und Lärm sind zu dulden.

5. SCHUTZ DER HEIMISCHEN INSEKTEN / IMMISSIONSCHUTZ BELEUCHTUNG
Bei der Außenbeleuchtung sollen ausschließlich insektenunschädliche Lampen (LED Lampen) verwendet werden.
Bei der Beleuchtung von privaten Flächen sind abgeschirmte Leuchten zu verwenden, deren Leuchtkegel in Richtung Boden ausgerichtet ist. Zulässig ist eine Beleuchtungsstärke von max. 5 Lux. Leuchten zu Dekorationszwecken wie beispielsweise Kugellampen und Strahler, die Bäume, Fassaden oder Fahnen beleuchten sind unzulässig. Ausgenommen ist dabei explizit die Weihnachtsbeleuchtung. Leuchtmittel mit weniger als 50 Lumen bleiben hierbei außer Betracht.

6. PFLANZUNG IM BEREICH VON LEITUNGEN UND KANÄLEN
Hinsichtlich geplanter Baumpflanzungen ist das „Merkblatt Bäume, unterirdische Leitungen und Kanäle“ der Forschungsgesellschaft für Straßen- und Verkehrswesen, Ausgabe 2013 - siehe u. a. Abschnitt 6 zu beachten.

7. INSEKTENFREUNDLICHES ALDERSBACH
- Lose Stein-/Materialschüttungen (sog. Schottergärten) und Plastikvliesabdeckungen sind nicht zugelassen
- Auf Art. 7 der Bayerischen Bauordnung wird hingewiesen

8. DENKMALSCHUTZ
Bei Bau- oder Grabungsarbeiten eventuell zu Tage tretende Bodendenkmäler unterliegen der Meldepflicht an das Bayerische Landesamt für Denkmalpflege oder die Untere Denkmalschutzbehörde gemäß Art. 8Abs. 1-2 BayDSchG.

9. SCHALLSCHUTZ
Die den schalltechnischen Festsetzungen zu Grunde liegenden Untersuchungen, können bei der Gemeinde zu den regulären Öffnungszeiten (telefonische Terminvereinbarung wird empfohlen) eingesehen werden.

PRÄAMBEL

Die Gemeinde Aldersbach erlässt den Bebauungsplan „Schwaig X“ mit Grünordnungsplan als Satzung auf Grundlage folgender Rechtsvorschriften:

Rechtsgrundlagen der planungsrechtlichen Festsetzungen:
§§ 2, 9 und 10 des BauGesetzBuches (BauGB) zuletzt geändert am 08.08.2020); Verordnung über die bauliche Nutzung der Grundstücke (BauNVO) i.d.F. der Bekanntmachung vom 21.11.2017.
Rechtsgrundlagen der bauordnungsrechtlichen Festsetzungen:
Art. 81 der Bayerischen BauOrdnung (BayBO) i.d.F. der Bekanntmachung vom 14.08.2007 (GVBI S. 588), zuletzt geändert am 24.07.2020.
Art. 23 der GemeindeOrdnung für den Freistaat Bayern i.d.F. der Bekanntmachung vom 22.08.1998 (GVBI S. 796ff), zuletzt geändert am 24.07.2020.
Rechtsgrundlagen der naturschutzrechtlichen Festsetzungen:
§7 bis 12, 13b und 13d Bayer. NaturSchutzGesetz (BayNatSchG) in der Fassung der Bekanntmachung vom 23.02.2011, zuletzt geändert am 21.02.2020;
§21 Abs. 1 BundesNaturSchutzGesetz (BNatSchG) in der Fassung der Bekanntmachung vom 29.07.2009, zuletzt geändert am 19.06.2020
PlanZeichenVerordnung 1990 (PlanZV 90) vom 18.12.1990, zuletzt geändert am 04.05.2017.

Der Geltungsbereich des Bebauungsplans umfasst die Flurstücke Fl.Nr. 312 und 312/4 mit einer Gesamtfläche von ca. 34.650m². Der Bebauungsplan besteht aus dem Plan mit Festsetzungen durch Planzeichen und Text, der Begründung und dem Umweltbericht.

VERFAHRENSVERMERKE

1. Der Gemeinderat hat in der Sitzung vom 00.00.0000 gemäß § 2 Abs. 1 BauGB die Aufstellung des Bebauungsplans beschlossen.
Der Aufstellungsbeschluss wurde am ____________ ortsüblich bekannt gemacht.

2. Die frühzeitige Öffentlichkeitsbeteiligung gemäß § 3 Abs. 1 BauGB mit öffentlicher Darlegung und Anhörung für den Vorentwurf des Bebauungsplans in der Fassung vom 00.00.0000 hat in der Zeit vom 00.00.0000 bis 00.00.0000 stattgefunden.

3. Die frühzeitige Beteiligung der Behörden und sonstigen Träger öffentlicher Belange gemäß § 4 Abs. 1 BauGB für den Vorentwurf des Bebauungsplans in der Fassung vom 00.00.0000 hat in der Zeit vom 00.00.0000 bis 00.00.00000 stattgefunden.

4. Zu dem Vorentwurf des Bebauungsplans in der Fassung vom 00.00.0000 wurden die Behörden und sonstigen Träger öffentlicher Belange gemäß § 4 Abs. 2 BauGB in der Zeit vom --.--.----- bis --.--.---- beteiligt.

5. Der Vorentwurf des Bebauungsplans in der Fassung vom 00.00.0000 wurde mit der Begründung gemäß § 3 Abs. 2 BauGB in der Zeit vom --.--.----- bis --.--.----- öffentlich ausgelegt.

6. Die Stadt/Gemeinde hat mit Beschluss des Stadt-/Gemeinderats vom ________ den Bebauungsplan gem. § 10 Abs. 1 BauGB in der Fassung vom --.--.----- als Satzung beschlossen.

Aldersbach, den ____________

1. Bürgermeister Harald Mayrhofer — Siegel

7. Die Regierung/Das Landratsamt hat den Bebauungsplan mit Bescheid vom ………. AZ ………. gemäß § 10 Abs. 2 BauGB genehmigt.

Siegel Genehmigungsbehörde — Siegel

8. Ausgefertigt

Aldersbach, den ____________

1. Bürgermeister Harald Mayrhofer — Siegel

9. Die Erteilung der Genehmigung des Bebauungsplans wurde am ___________ gemäß § 10 Abs. 3 Halbsatz 1 BauGB/Der Satzungsbeschluss zu dem Bebauungsplan wurde am ______________ gemäß § 10 Abs. 3 Halbsatz 2 BauGB ortsüblich bekannt gemacht. Der Bebauungsplan mit Begründung wird seit diesem Tag zu den üblichen Dienststunden in der Gemeinde zu jedermanns Einsicht bereitgehalten und über dessen Inhalt auf Verlangen Auskunft gegeben. Der Bebauungsplan ist damit in Kraft getreten. Auf die Rechtsfolgen des § 44 Abs. 3 Satz 1 und 2 sowie Abs. 4 BauGB und die §§ 214 und 215 BauGB wurde in der Bekanntmachung hingewiesen..

Aldersbach, den ____________

1. Bürgermeister Harald Mayrhofer

BEBAUUNGSPLAN "SCHWAIG X" ALDERSBACH

-VORENTWURF-

Gemeinde:	Aldersbach
Landkreis:	Passau
Reg.Bezirk:	Niederbayern

Stand der Planung:	07.08.2024
Maßstab	1:1000
Planverfasser Bebauungsplan:	**Arc Architekten Partnerschaft mbB** Manfred Brennecke Volker Kilian Stefan Kohlmeier Michael Leidl Florian Riesinger Alfons-Hundsrucker-Str. 11 84364 Hirschbach